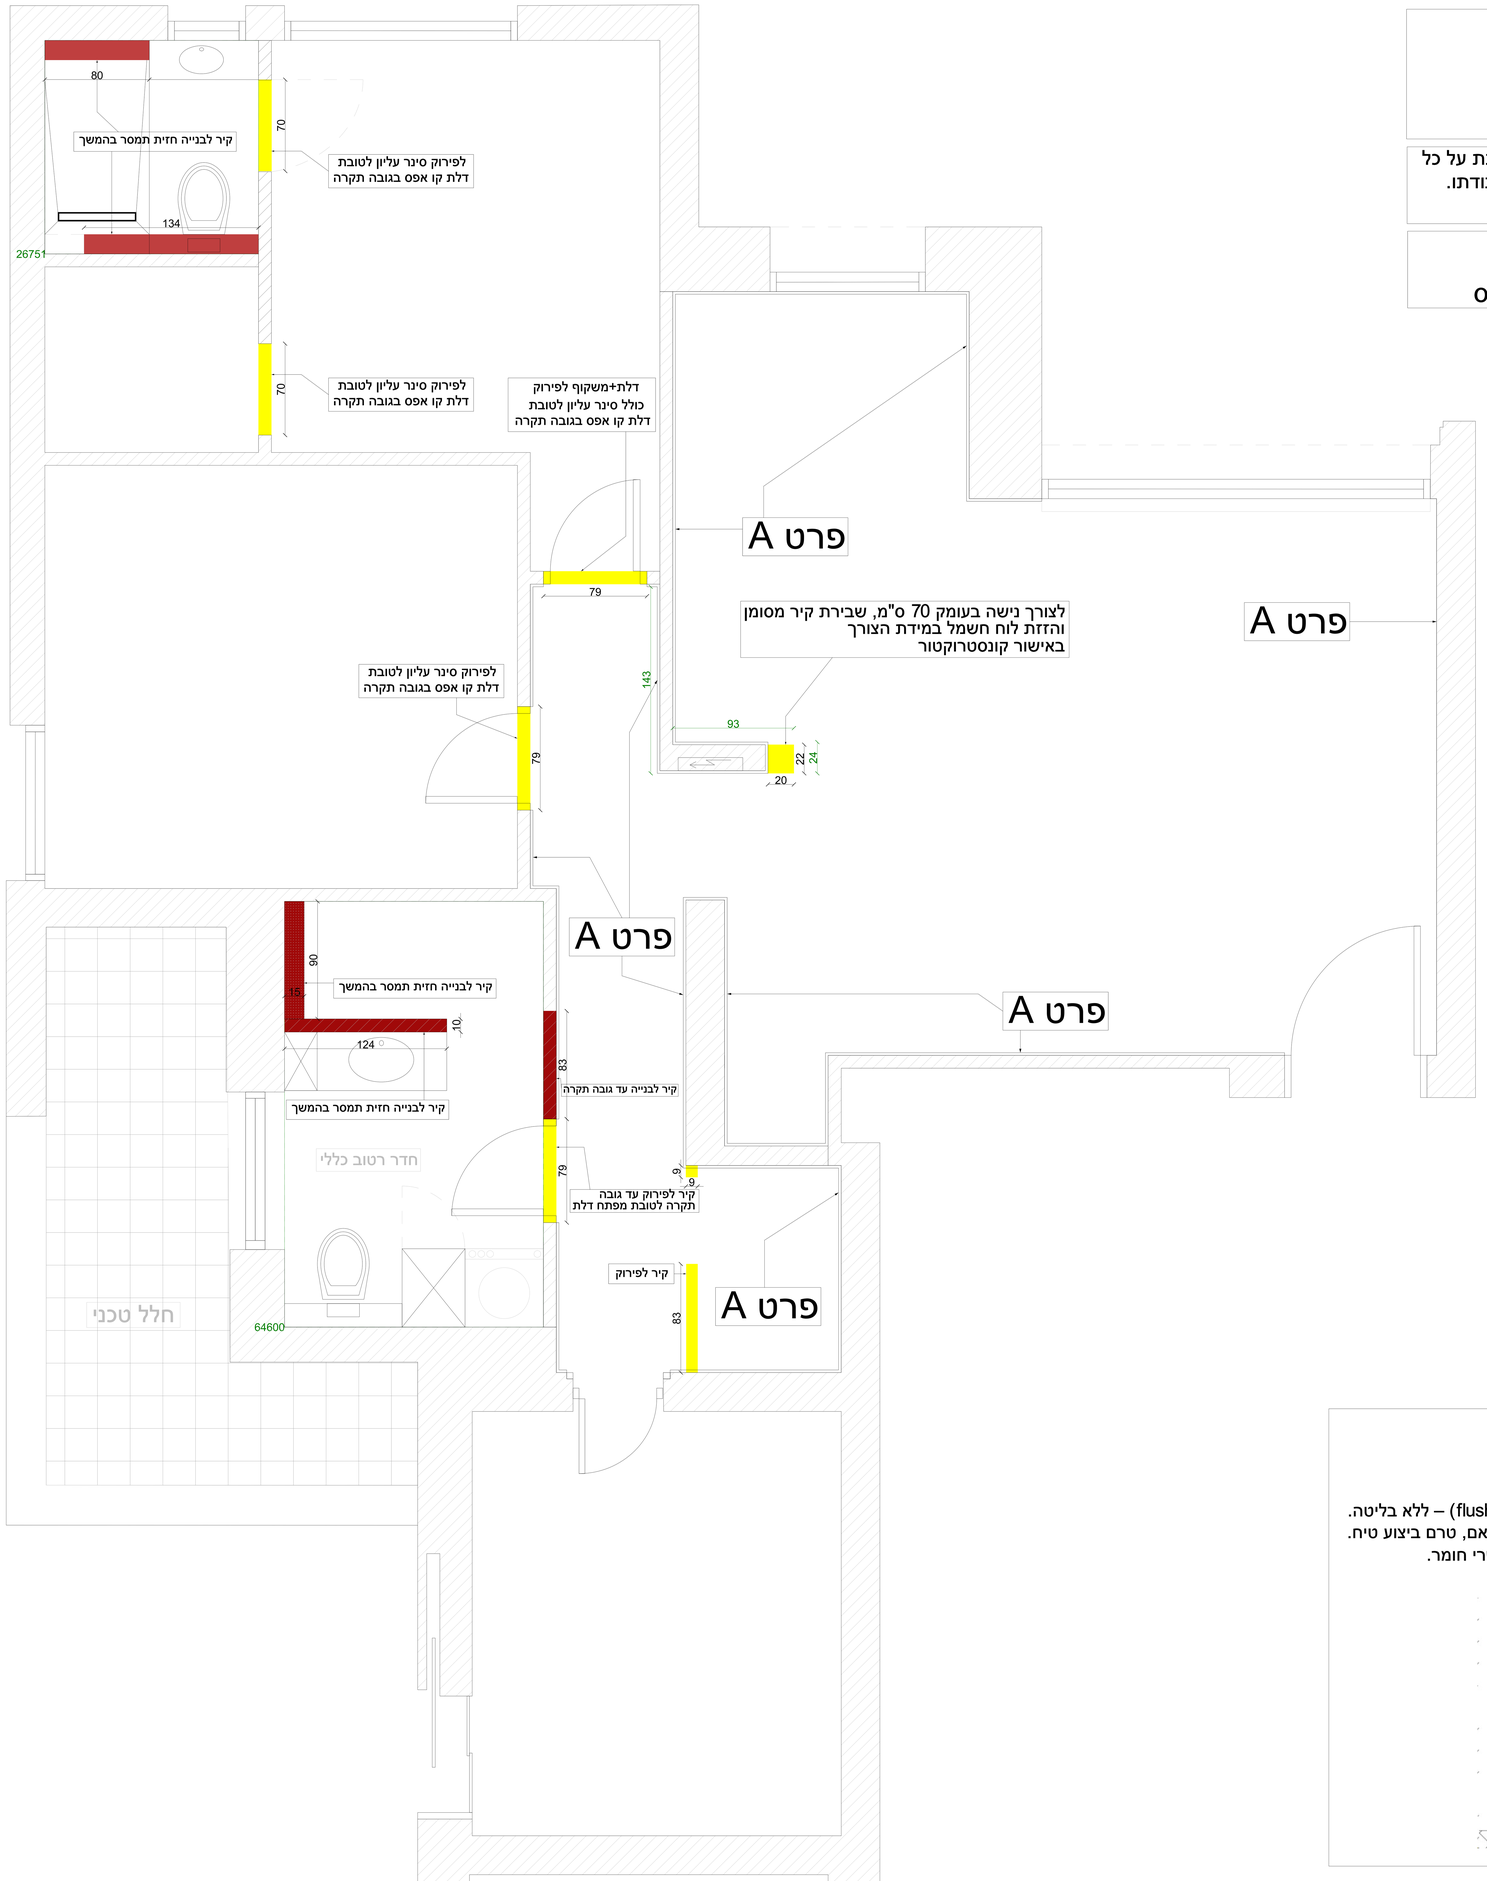

הערות:

אין לפגוע או להרוס אלמנט קונסטרוקטיבי כלשהו
במהלך עבודות הפירוק וההריסה
במידת הצורך יש לקבל יעוץ קונסטרוקטור
לפני ביצוע הפירוק ו\או ההריסה

הקבלן אחראי למידות ועליו לבקר אותן ולהודיע למתכננת על כל טעות, סטייה, סתירה או אי התאמה בטרם המשיך בעבודתו.
אין לקבוע גדלים ע"י מדידה מהתכניות

פירוק והריסה

בנייה בלוק/גבס

פרט A

הערת ביצוע – פאנל בקו אפס עם הטיח (שקוע):

- הפאנל יבוצע בשקיעה לקיר כך שייושר לקו הטיח (flush) – ללא בליטה.
- יש להכין שקיעה בעובי הפאנל בגבס או בבטון בהתאם, טרם ביצוע טיח.
- סיום טיח בקו מדויק עם הפאנל – טיח חלק, ללא גשרי חומר.

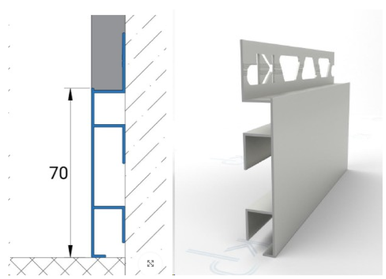

הפרוייקט:

משפחת פסלב

שם תכנית:

תוכנית פירוק והריסה + בנייה

תאריך:	קנ"מ:
01/01/25	1:50

לאישור	לביצוע	למכרז	לעיון
○	○	○	●

מספר גליון:

הערות:

שינויים ועדכונים:

תאריך	מס'	מהות השינוי\עדכון
	1	
	2	
	3	
	4	
	5	
	6	
	7	

=המבצע אחראי לבדיקת התכניות ולהתאמתן במקום!
=על המבצע לבקר את כל המידות ועל כל טעות או אי התאמה עליו להודיע למתכנן.
=אין לקבוע מידות על ידי מדידה בשירטוט!
=תכנית זו הינה תכנית עיצובית בלבד לטובת מיקום אלמנטים בחלל, מידות וחומרים ואינה משמשת תכנית הנדסית \ קונסטרוקטיבית
=על המבצע+המזמין יש להזמין מהנדס מוסמך לכל תחום בתכנית(כגון מהנדס בניין\קונסטרוקטור\ מהנדס חשמל וכו..)
כולל בדיקות במהלך העבודה וחתימה בסיומה
=במידה ואין חתימת מהנדס\קונסטרוקטור\ מהנדס חשמל וכו.. האחריות המקצועית והחוקית הינה על המבצע בלבד!
=מהנדס ו\או יועץ אשר שמו חתום בתכנית זו נושא לבדו באחריות המקצועית והחוקית לתכנית
=אין לעשות כל שימוש בתכנית זו או ברעיונות הגלומים בה ללא אישור בכתב מהמתכנן

ליאונה בן-סימון | עיצוב פנים
050-6770927
Lionafeldman15@gmail.com

LIONA B. SIMON
INTERIOR DESIGN